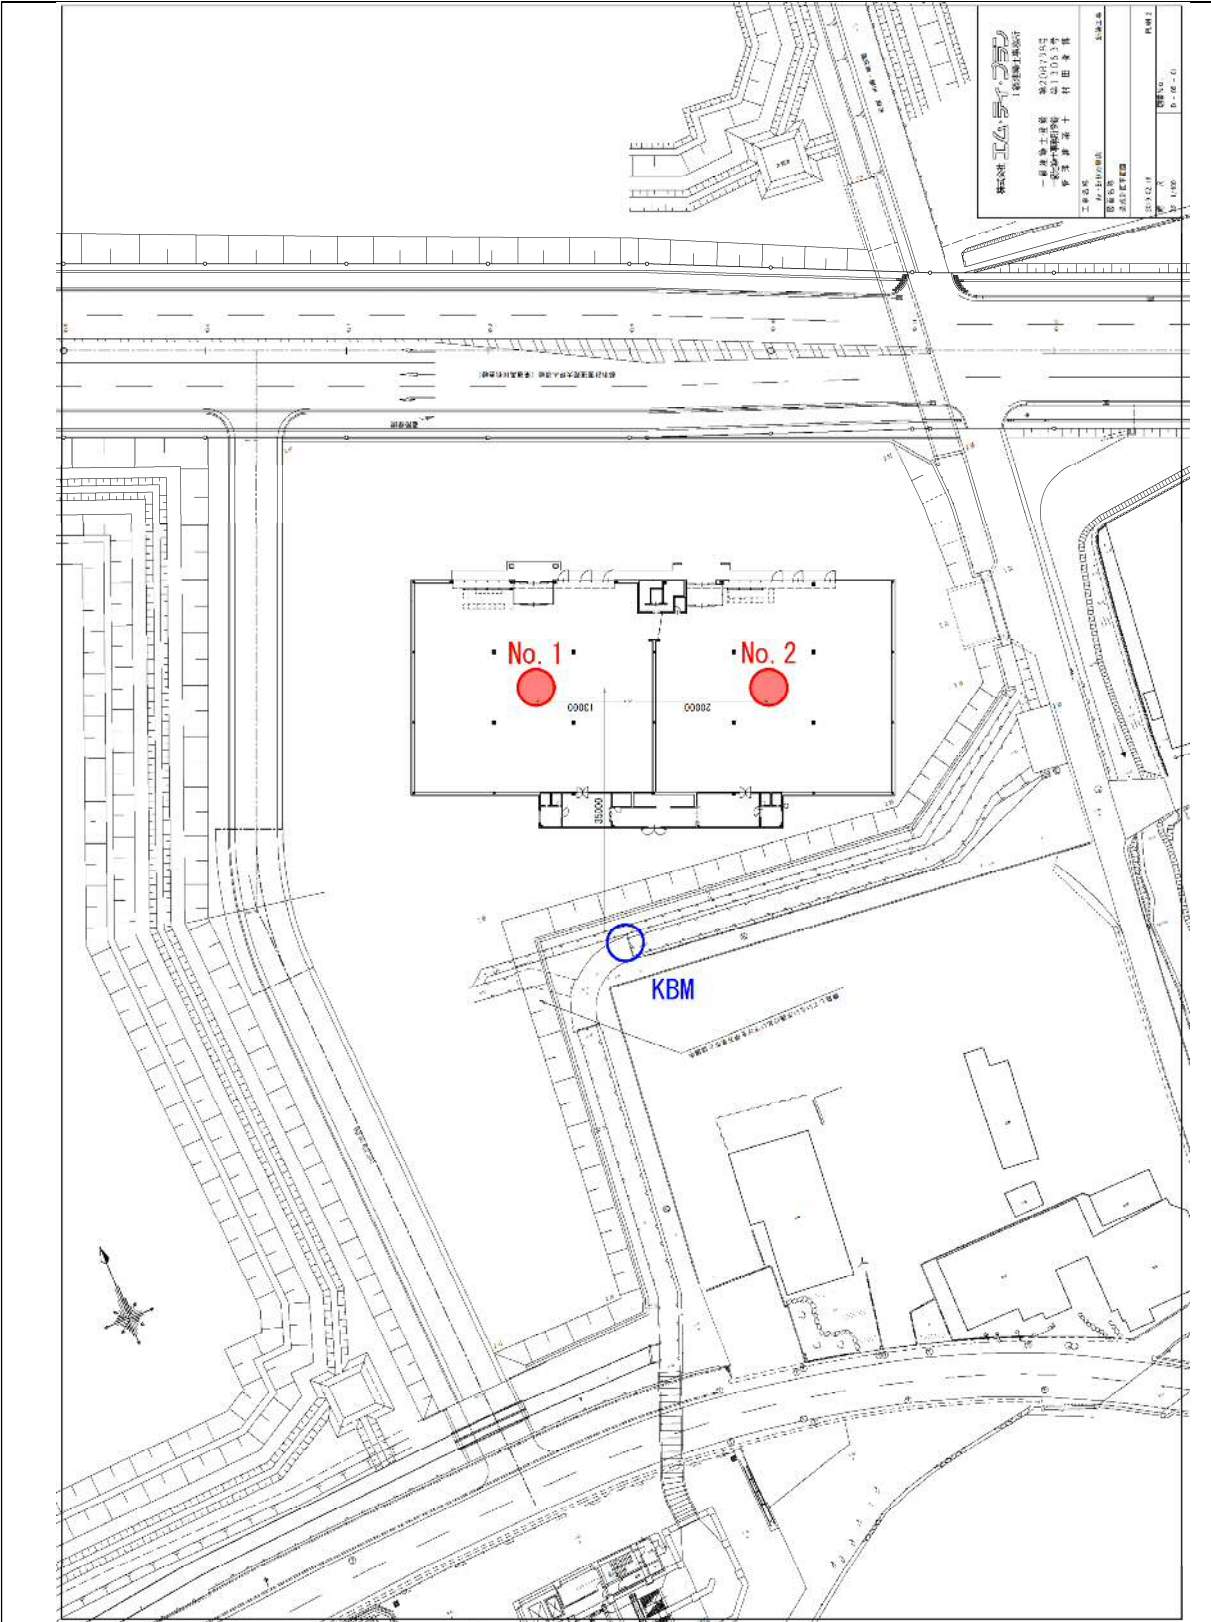




ボーリング調査位図

縮尺 任意

凡例 ● 調査箇所

 
 
 
ボーリング柱状図

調査名 調査ボーリング

ボーリングNo

事業・工事名 A v ・ B r 伊万里店新築工事

シート No

ボーリング名	No. 1		調査位置		佐賀県伊万里市松島町					北緯		
発注機関	(株)エム・ティ・プラン				調査期間		平成 31年 2月 26日 ~ 31年 2月 27日			東経		
調査業者名	新栄地研株式会社 電話 (0952-32-0916)		主任技師		現代場人		コ鑑ア者		古賀優一		ボーリング責任者	嶋田賢一郎
孔口標高	+3.22m	角  度	方  向	地盤勾配 	使用機種	試錐機		東邦 D-0		ハンマー落下用具	半自動落下式	
総掘進長	13.00m					エンジン		NFD-10		ポンプ	SP-30	

[illegible]

コア写真

調査ボーリング No.1 標高 +3.22m ~ -10.78m



ボーリング柱状図

調査名 調査ボーリング

ボーリングNo

事業・工事名 Av・Br伊万里店新築工事

シート No

ボーリング名	No. 2		調査位置		佐賀県伊万里市松島町						北緯				
発注機関	(株)エム・ティ・プラン				調査期間		平成 31年 2月 28日 ~ 31年 3月 1日				東経				
調査業者名	新栄地研株式会社 電話 (0952-32-0916)		主任技師		現 場 人		コ 鑑 定 者		古賀優一		ボーリング 責 任 者		嶋田賢一郎		
孔 口 標 高	+3.17m	角 度	180° 上 90° 下 0°	方 向	北 0° 270° 西 90° 東 180° 南	地盤 勾配	鉛直 水平0° 90°	使用 機種	試 錐 機		東 邦 D - 0		ハンマー 落下用具	半 自 動 落 下 式	
総 掘 進 長	13.00m								エ ン ジ ン		N F D - 1 0			ポ ン プ	

[illegible]

コア写真

調査ボーリング No.2 標高 +3.17m ~ -9.83m

